
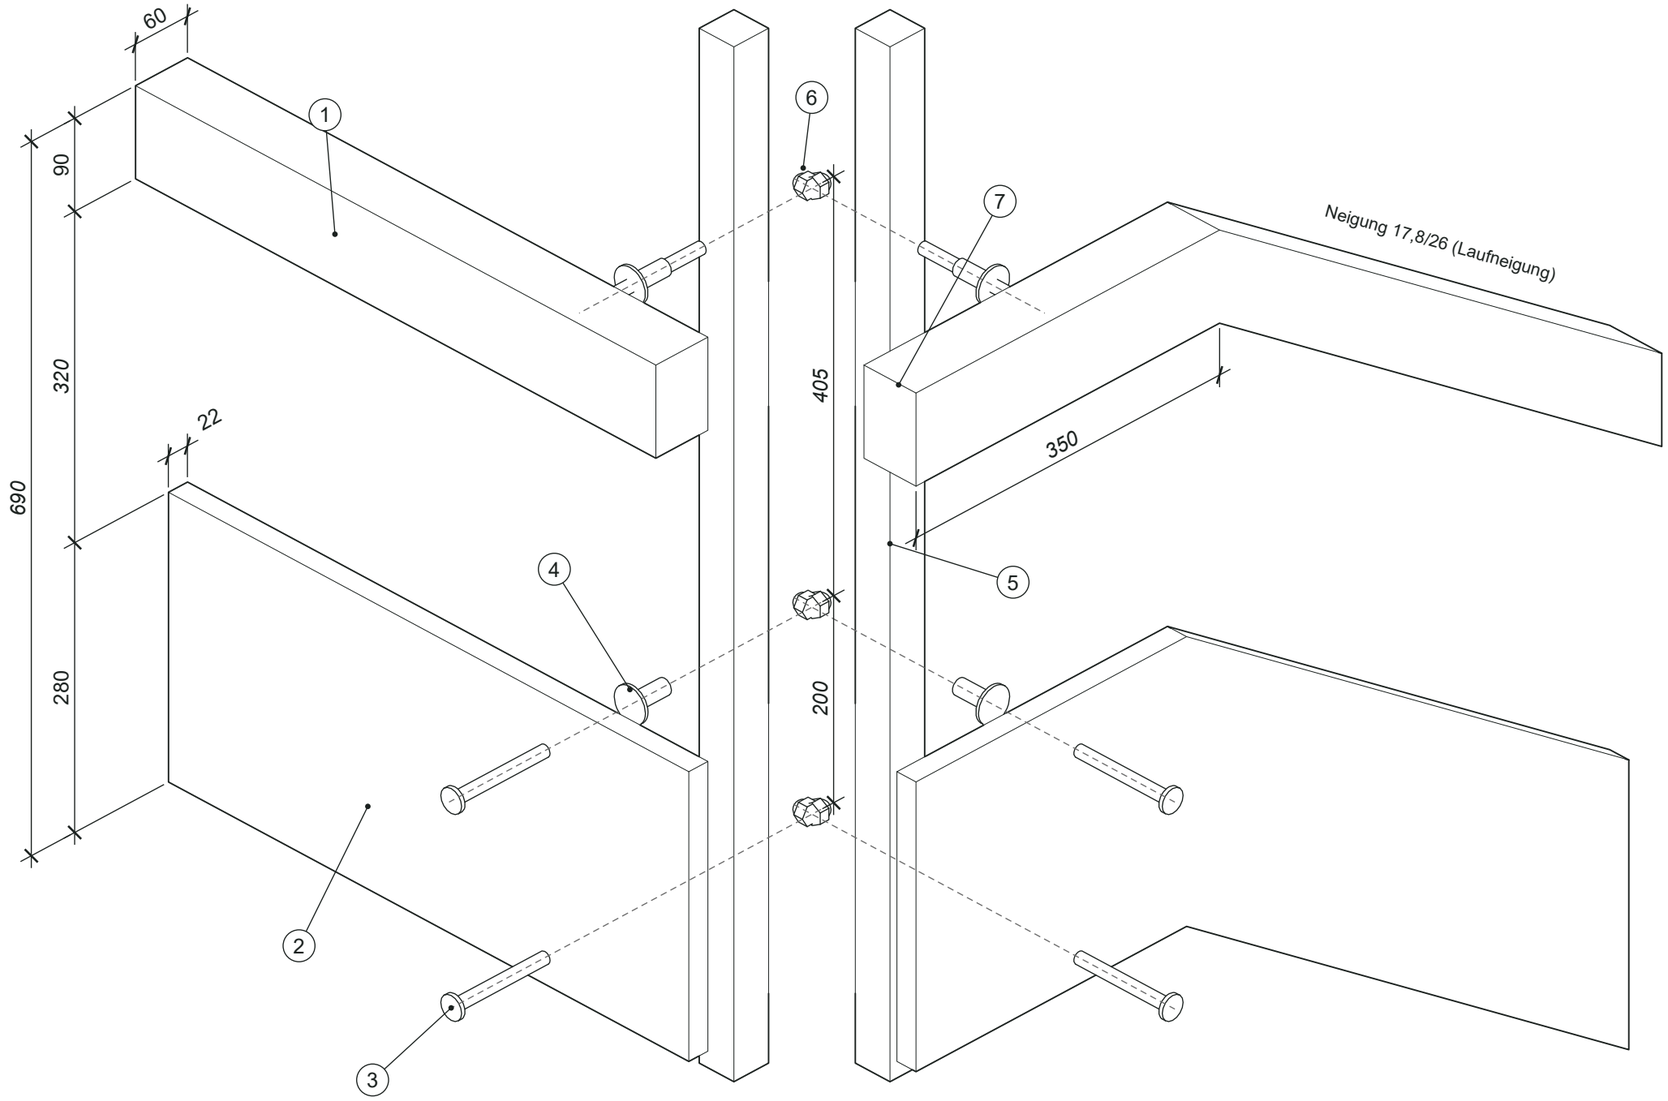


Axonometrie (Explosion) M 1:5

Ecke Deckenrand OG1 / Lauf 3, Blick von der Treppe – Maßzahlen = wahre Längen

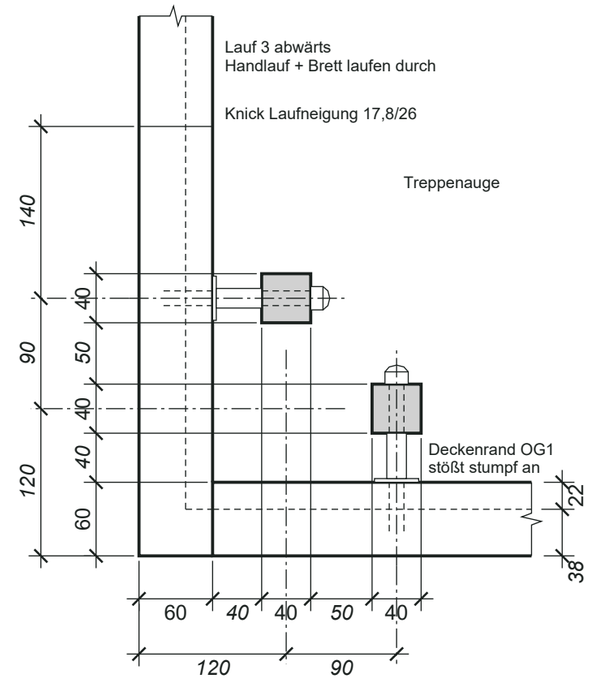

Draufsicht Einbauzustand M 1:5

Bolzen in Höhe Handlaufmitte, Brett verdeckt

Maßstabswahl
Detail in der Bildebene (gemessen): 1245 × 875 mm
Zeichenfläche A3: 390 × 277 mm (Rand 20/10)
– Schriftfeld/Draufsicht: frei ≈ 270 × 185 mm
1:2 → 623 × 438 mm passt nicht
1:2,5 → 498 × 350 mm passt nicht
1:5 → 249 × 175 mm passt (+ Maßketten ≈ 262 × 182 mm)
1:10 → 125 × 88 mm passt, aber Bauteile 22 mm → 2,2 mm, zu klein
Gewählt: 1:5 (größter passender Normmaßstab)

0 50 100 150 200 mm

Positionen
1 Handlauf Teak 60/90
2 Brüstungsbrett Teak 280/22
3 Linsenkopfschraube M12, Edelstahl
4 Rosette Ø36 + Distanzhülse Ø16, Edelstahl
5 Pfosten Stahl □ 40/40, schwarz, paarweise
6 Hutmutter M12, Edelstahl
7 Eckstoß stumpf: Brett + Handlauf Lauf 3 laufen durch

Hinweise
Maße in mm. Maßzahlen gerade = in der Vorlage beschriftet, *kursiv = aus der PDF-Vektorgeometrie gemessen/abgeleitet.*
Axonometrie: senkr. Parallelprojektion, 45° gedreht; Achsen x/y unter 28,2°, Verkürzung x/y 0,803, z 0,844 (1:5 in der Bildebene).
Explosion: Holzteile 120 mm von den Pfosten abgerückt.
Pfosten oben/unten gekürzt (dargestellt 1000). Kanten scharf, keine Radien. Hülse/Rosette in der Vorlage angenommen.

Geländerecke Treppenauge – Bemaßung

Ecke Deckenrand OG1 / Lauf 3 · Grundlage: Detailmappe Treppe Kern 335, Bl. 2

Projekt	Ort	Vorlage
Bachelorthesis „Der Anfang“	TIB, Treppenkern 335	Jan Andis Böhm
Maßstab	**Format**	**Datum**
1:5	A3 (420 × 297)	25.10.2026